


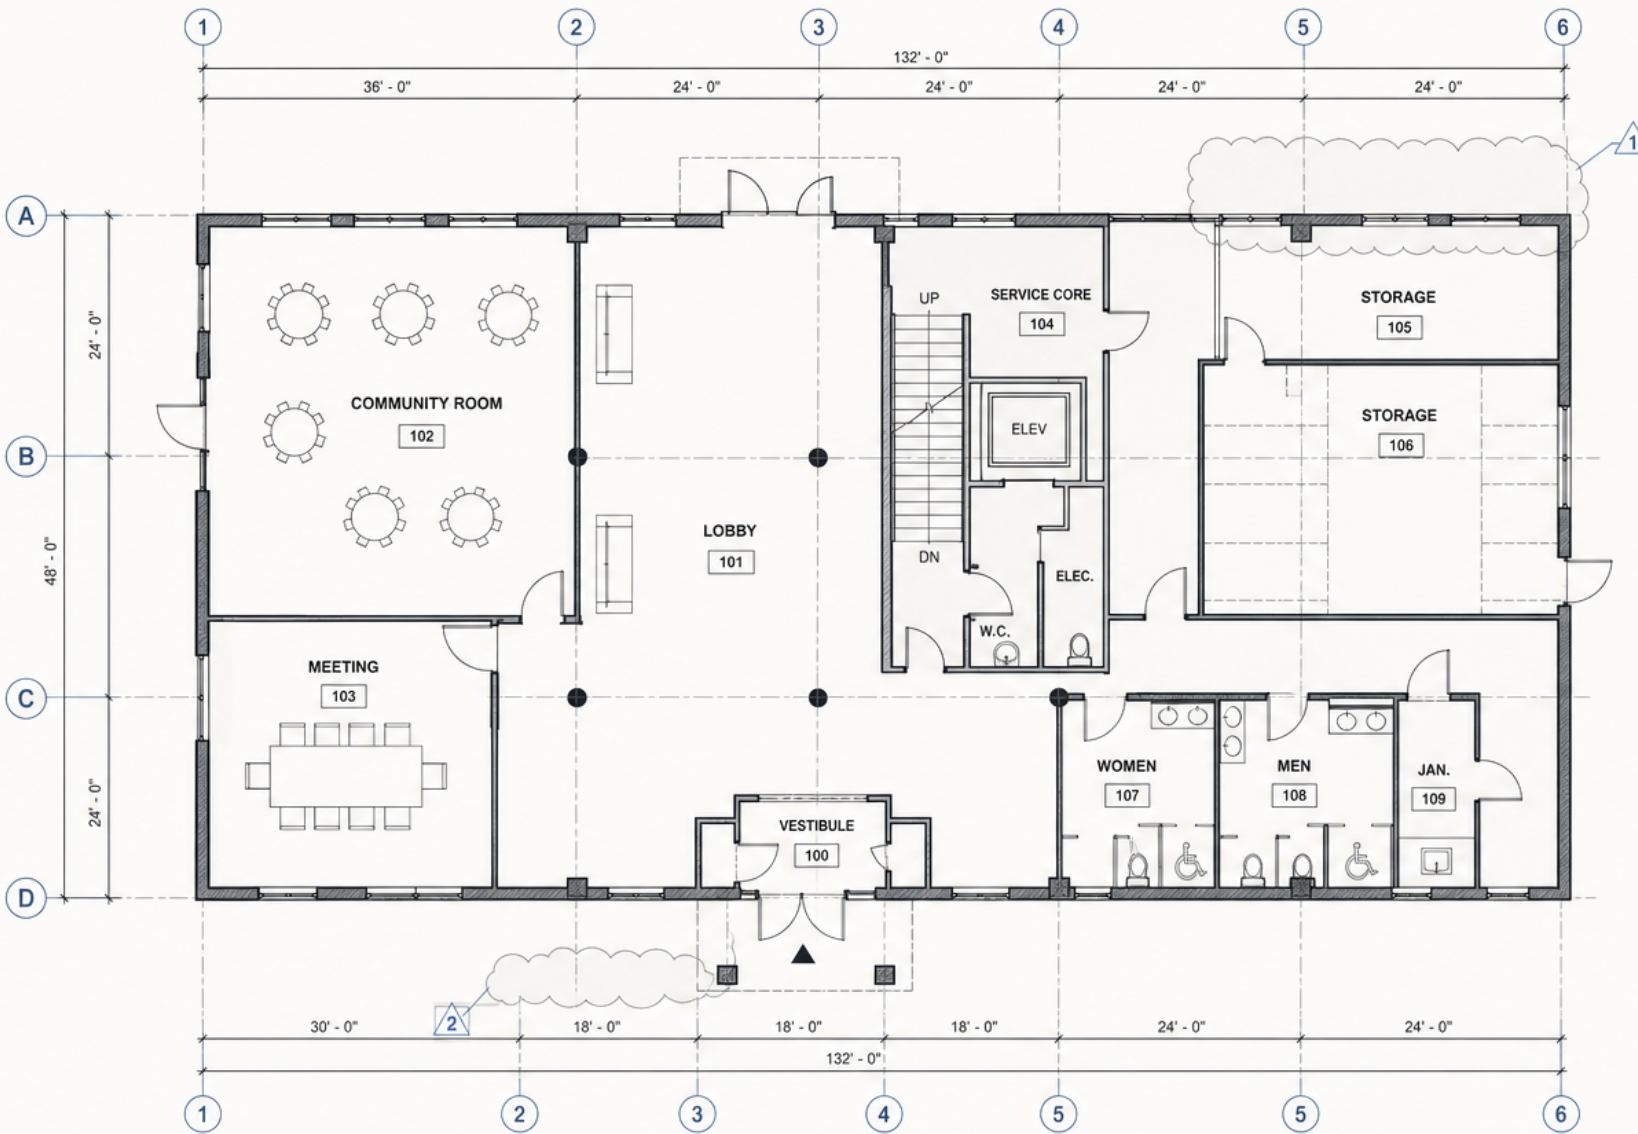

PLAN LEGEND	
	EXTERIOR WALL
	INTERIOR WALL
	COLUMN
	DOOR
	WINDOW
	REVISION CLOUD

REVISION SCHEDULE		
MARK	DATE	DESCRIPTION
1	2026-07-15	EXTENT OF CANOPY REVISED
2	2026-07-22	ENTRY STEPS AND PORCH REVISED

- GENERAL NOTES**
- DIMENSIONS ARE TO FACE OF STUD OR FACE OF CONCRETE UNLESS NOTED OTHERWISE.
 - DO NOT SCALE DRAWINGS.
 - VERIFY ALL DIMENSIONS AND CONDITIONS IN THE FIELD PRIOR TO CONSTRUCTION.
 - REPORT DISCREPANCIES TO ARCHITECT PRIOR TO PROCEEDING.

**HARBOR BUILD
PROJECT BETA**
DESIGN PHASE

GROUND FLOOR PLAN

PROJECT NO.	HB-PB-26
DRAWN BY	---
CHECKED BY	---
DATE	2026-07-29
SCALE	1/8" = 1'-0"

PROJECT BETA
A1.10
PRELIMINARY
2026-07-29

1 GROUND FLOOR PLAN
1/8" = 1'-0"

HARBOR BUILD

PROJECT BETA

DESIGN PHASE

FOUNDATION LAYOUT

GENERAL NOTES:

1. REFER TO SHEET S0.01 FOR GENERAL NOTES.
2. ALL FOOTINGS CENTERED ON COLUMNS AND PIERS UNO.
3. TOP OF FOOTINGS @ EL. 100'-0" UNO.
4. SEE SHEET S1.01 FOR FOUNDATION DETAILS.


LEGEND:


-  SPREAD FOOTING
-  PIER
-  GRADE BEAM / FOUNDATION WALL
-  ELEVATOR PIT
-  SERVICE TRENCH (REFERENCE)

S1.02

PRELIMINARY

2026-07-29

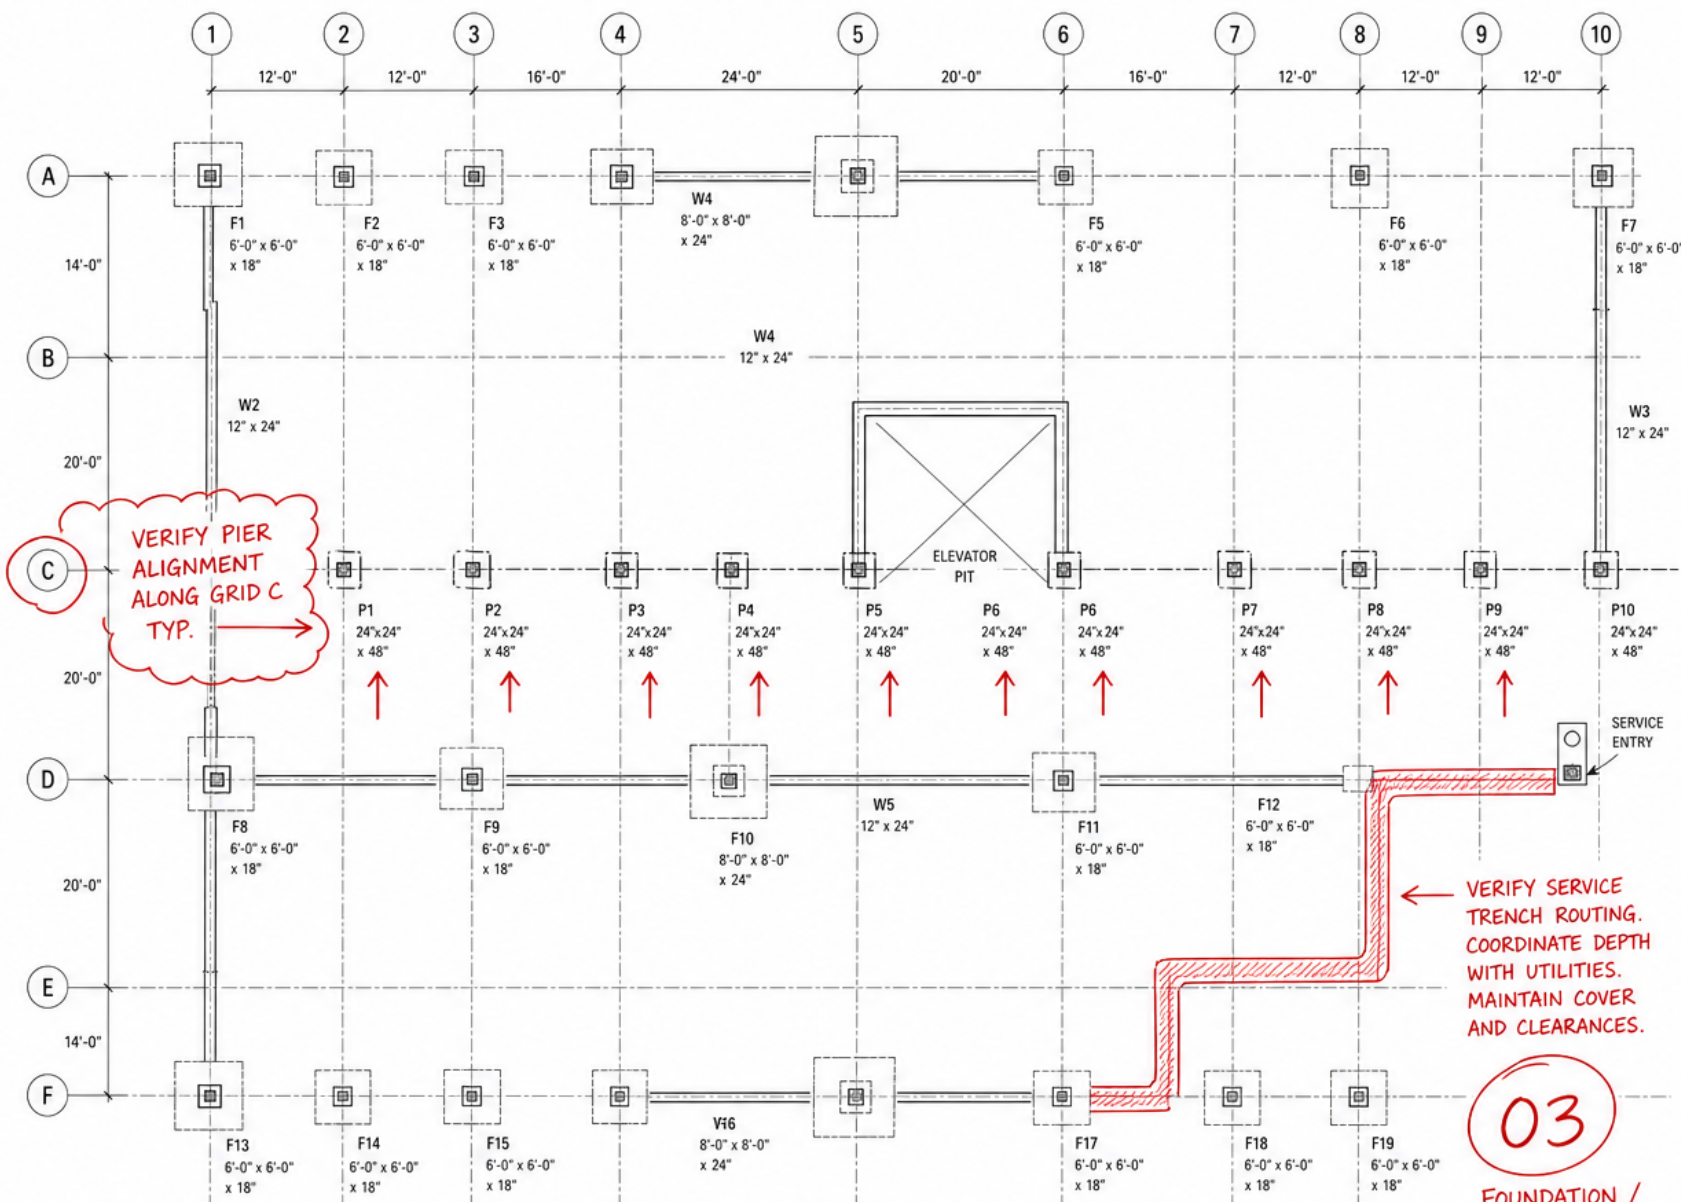

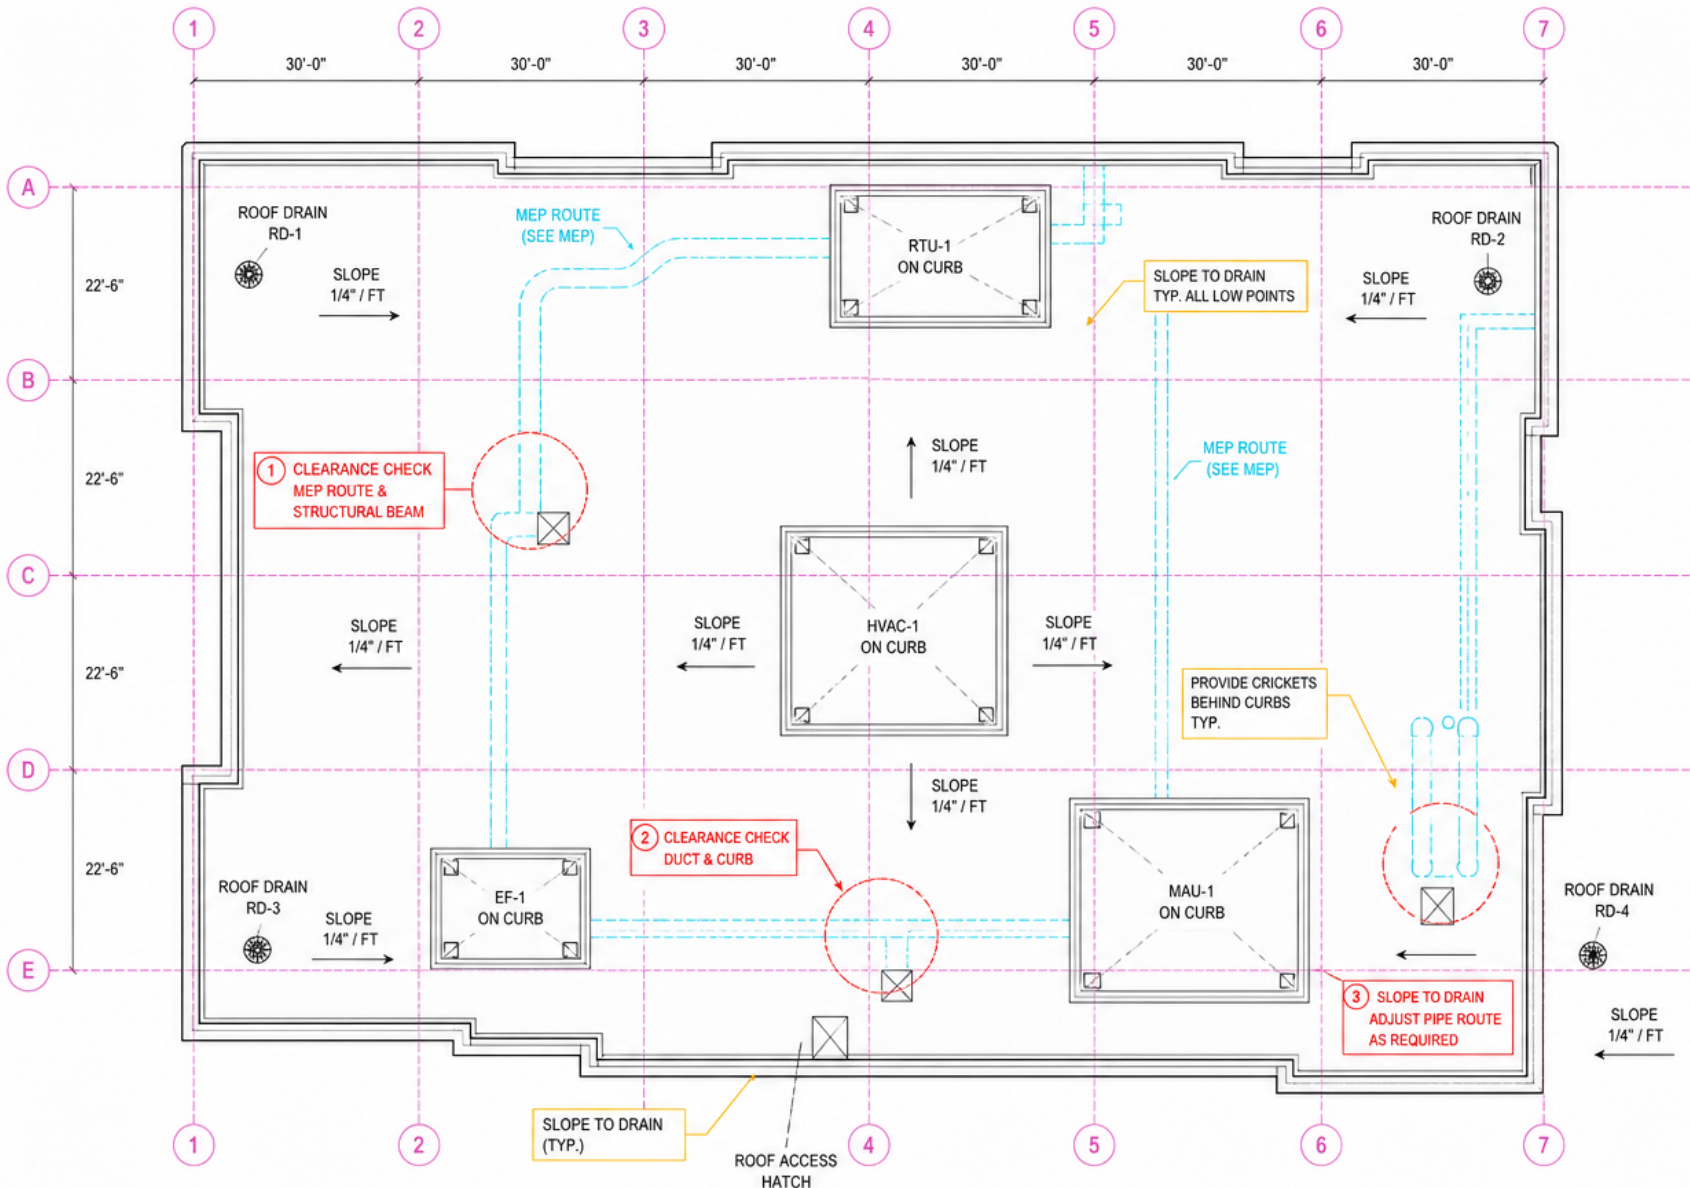

ROOF PLAN


GENERAL NOTES

1. REFER TO ARCHITECTURAL SHEETS FOR ROOFING ASSEMBLY AND DETAILS.
2. REFER TO STRUCTURAL SHEETS FOR ROOF FRAMING AND EQUIPMENT SUPPORT.
3. REFER TO MEP SHEETS FOR EQUIPMENT AND ROUTING INFORMATION.
4. COORDINATE ALL PENETRATIONS AND OPENINGS.

LEGEND

- ARCHITECTURAL (ROOF)
- - - MEP ROUTE (COORDINATION)
- - - STRUCTURAL GRID
- DRAINAGE / SLOPE CALLOUT
- COORDINATION CLASH

KEY PLAN

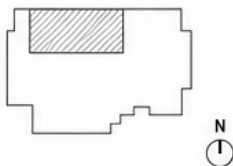

REVISION SCHEDULE

NO.	DATE	DESCRIPTION

PROJECT BETA
ROOF COORDINATION

A1.41

PRELIMINARY

2026-07-29

SCALE: 1/8" = 1'-0"